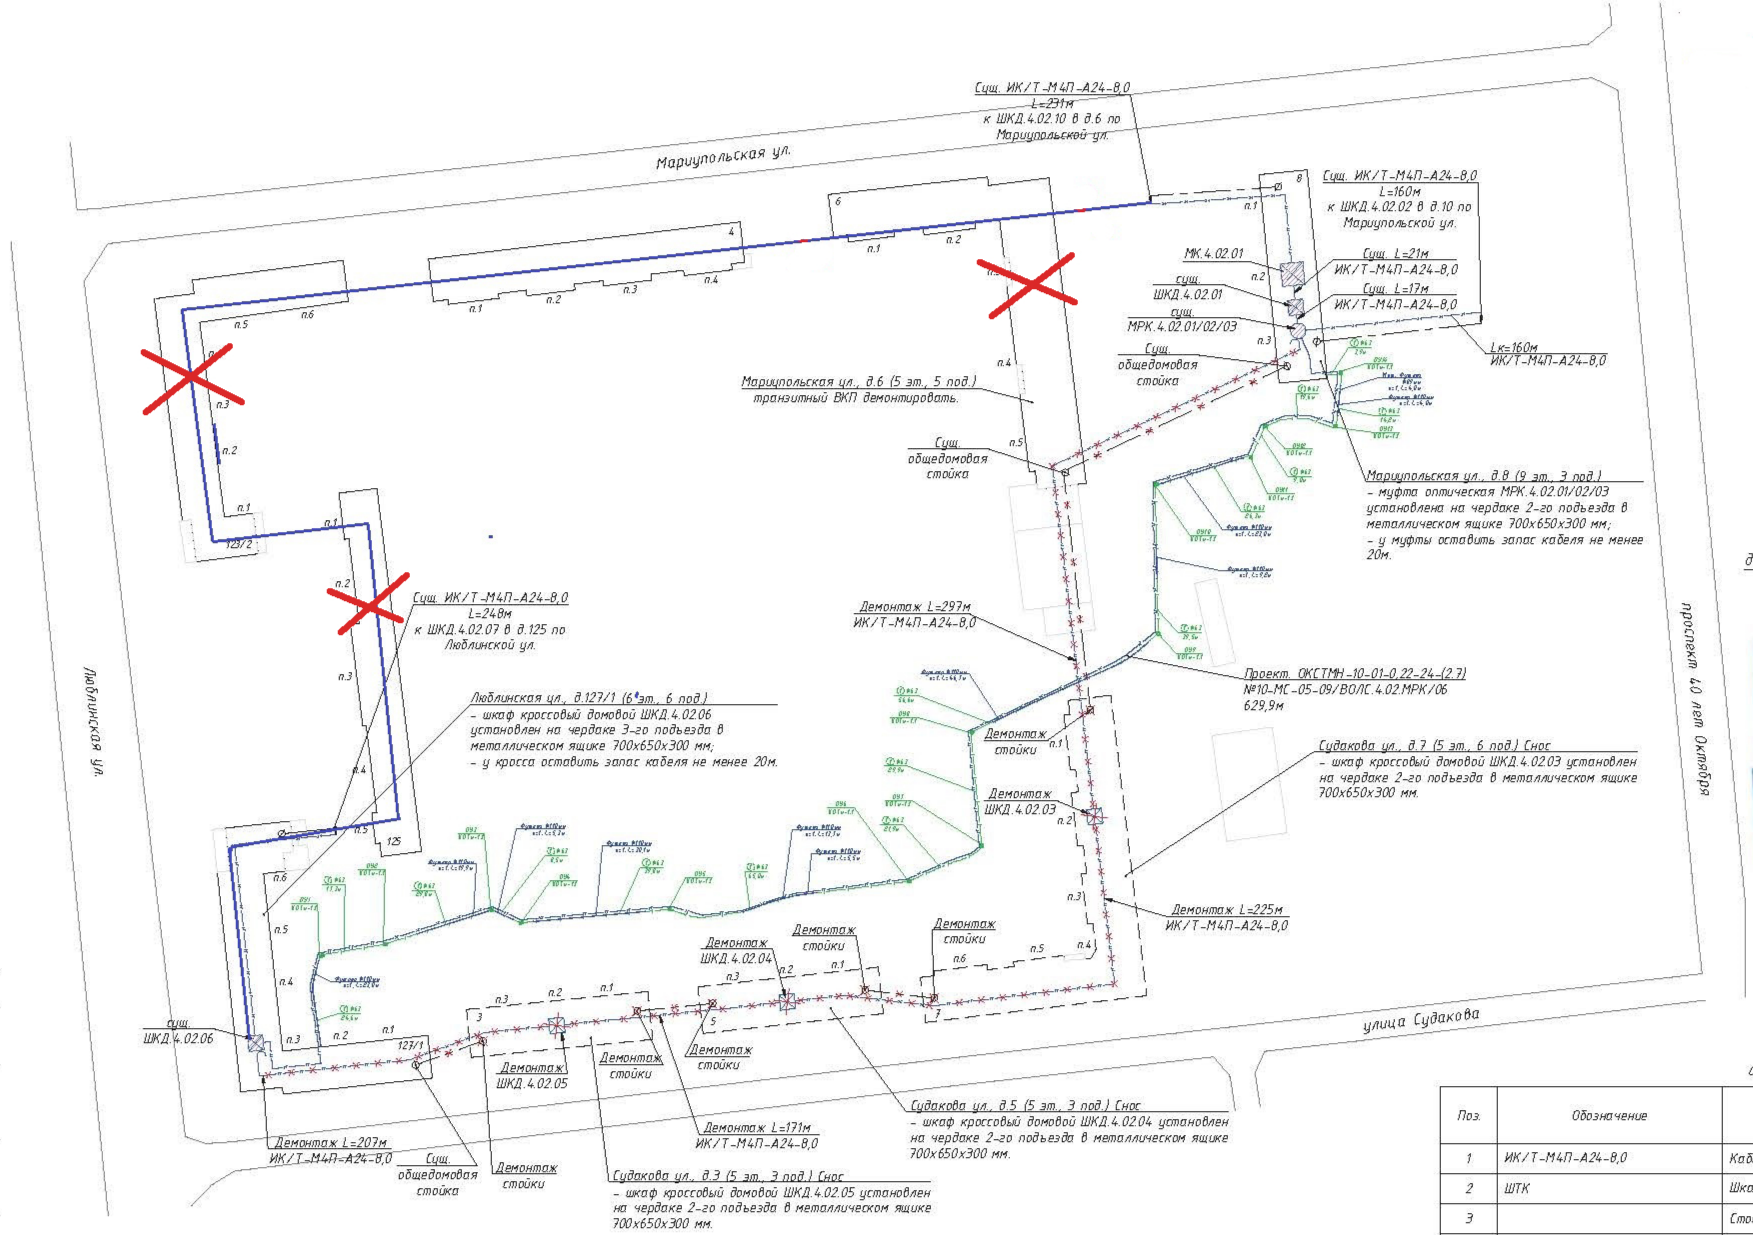

Сущ. ИК/Т-М4П-А24-8,0
L=231м
к ШКД.4.02.10 в д.6 по Мариупольской ул.

Сущ. ИК/Т-М4П-А24-8,0
L=160м
к ШКД.4.02.02 в д.10 по Мариупольской ул.

Сущ. L=21м
ИК/Т-М4П-А24-8,0

Сущ. L=17м
ИК/Т-М4П-А24-8,0

Lк=160м
ИК/Т-М4П-А24-8,0

Мариупольская ул., д.6 (5 эт., 5 под.)
транзитный ВКП демонтировать.

Мариупольская ул., д.8 (9 эт., 3 под.)
- муфта оптическая МРК.4.02.01/02/03 установлена на чердаке 2-го подъезда в металлическом ящике 700х650х300 мм;
- у муфты оставить запас кабеля не менее 20м.

Сущ. ИК/Т-М4П-А24-8,0
L=248м
к ШКД.4.02.07 в д.125 по Люблинской ул.

Люблинская ул., д.127/1 (6 эт., 6 под.)
- шкаф кроссовый домовой ШКД.4.02.06 установлен на чердаке 3-го подъезда в металлическом ящике 700х650х300 мм;
- у кросса оставить запас кабеля не менее 20м.

Демонтаж L=297м
ИК/Т-М4П-А24-8,0

Проект. ОКСТМН-10-01-0,22-24-(2.7)
№10-МС-05-09/ВОЛС.4.02.МРК/06
629,9м

Судакова ул., д.7 (5 эт., 6 под.) Снос
- шкаф кроссовый домовой ШКД.4.02.03 установлен на чердаке 2-го подъезда в металлическом ящике 700х650х300 мм.

Демонтаж L=225м
ИК/Т-М4П-А24-8,0

Судакова ул., д.5 (5 эт., 3 под.) Снос
- шкаф кроссовый домовой ШКД.4.02.04 установлен на чердаке 2-го подъезда в металлическом ящике 700х650х300 мм.

Демонтаж L=171м
ИК/Т-М4П-А24-8,0

Судакова ул., д.3 (5 эт., 3 под.) Снос
- шкаф кроссовый домовой ШКД.4.02.05 установлен на чердаке 2-го подъезда в металлическом ящике 700х650х300 мм.

Демонтаж L=207м
ИК/Т-М4П-А24-8,0

Условные обозначения:

- ▭ – существующее здания;
- ▭ – сносимое здания;
- ☒ – существующий кросс оптический;
- ● – существующая оптическая муфта;
- ═n═ – существующие оптические кабели с указанием количества волокон;
- —n— – проектируемый оптический кабель, прокладываемый в грунте, с указанием количества волокон;
- Ø— — —Ø – воздушно-кабельный переход;
- Ø – существующая стандартная стойка ВКП;
- —✕ 24 ✕— – демонтируемый кабель;
- —·—·— – проектируемая труба в грунте;
- —z—z— – существующая кабельная канализация;
- 🟩 – проектируемое поворотное устройство;
- ПУ-1 – номер поворотного устройства;
- 1 – количество каналов;
- 12,5 – длина между устройствами смотровыми.

д.127/1 - ПУ1	ПУ1 - ПУ14	ПУ14 - д.8
⊗ ОК	⊗ ОК	⊗ ОК

Согласовано.
Зарегистрировано 10-МС-05-09/ВОЛС.4.02.02(ВС)
За три дня до начала работ связаться с представителем эксплуатации для согласования порядка их выполнения
по тел. см. п.10 ТУ
Начальник (Петаев Г.А.)
Срок действия согласования 3 года, с 25.11.25

Публичное Акционерное Общество
Ростелеком
МАКРОРЕГИОНАЛЬНЫЙ ФИЛИАЛ "ЦЕНТР"
Московское городское управление технической эксплуатации
Отдел технического учета

Бирка кабеля:

ПАО "Ростелеком"
№10-МС-05-09/ВОЛС.4.02.МРК/06
ОКСТМН-10-01-0,22-24-(2.7)

1. Монтаж оптического кабеля марки ОКСТМН-10-01-0,22-24-(2.7) от сущ. шкафа в д. 127/1 по ул. Люблинская до сущ муфты разветвительной в д. 8 по ул. Мариупольская - 629,9 м, в том числе:
   - в грунте в трубе ТПЖГС d=63 мм (с учетом укладки и монтажа) - 405,9 м;
   - по зданиям (с учетом укладки, монтажа и запасов) - 184,0 м;
   - запас у кроссов - 40,0м.
2. Переварка волокон в сущ. кроссе и муфте в д. 127/1 по ул. Люблинская и д. 8 по ул. Мариупольская - 2 шт. (48 сварок).
3. Проведение измерений на 24-х волоконно-оптическом кабеле в двух направлениях - 3 шт. (72 волокна).
4. Демонтаж оптического кабеля ИК/Т-М4П-А24-8,0 от д. 127/1 по ул. Люблинская до д. 8 по ул. Мариупольская - 900,0 м;
5. Демонтаж элементов стойки ВКП для крепления волоконно-оптического кабеля - 6 шт.
6. Демонтаж ШКД - 3 шт.
7. Прокладку волоконно-оптического кабеля (ВОК) для выноса сетей ПАО «Ростелеком» выполнить в грунте в проектируемой трубе ТПЖГС Ф63 мм.
8. Работы по прокладке ВОК в грунте должны выполняться в соответствии с " Руководством по строительству линейных сооружений местных сетей связи". ВОК в устройствах смотровых уложить на проектируемые консоли и крепить пластиковыми стяжками. ВОК в устройствах смотровых и на входе в дом маркировать свинцовыми бирками с указанием марки кабеля, владельца и номера его телефона, а также адреса домов к которому проложен данный кабель.
9. Подъем оптического кабеля из подвала на чердак выполнить по существующему слаботочному стояку здания или по существующему стояку ПАО «Ростелеком».
10. ВОК по подвалу зданий проложить по существующим лоткам и закладным для слаботочных систем. Кабель крепить к лоткам пластиковыми стяжками через 1 м. В случае отсутствия существующих закладных, ВОК по чердакам и подвалам до места установки существующего оборудования прокладывается в металлорукаве диаметром 21 мм на тросе 2 мм с креплением к несущим конструкциям здания рым-гайками.
11. При прокладке ВОК по зданиям маркировать бирками с указанием марки кабеля, владельца и номера его телефона, а также адрес дома к которому проложен данный кабель.
12. При прокладке оптического кабеля выдерживать радиус изгиба не менее 20 его диаметров.

Московский фонд реновации жилой застройки
В ПРОИЗВОДСТВО РАБОТ
Начальник технического управления

Объем работ

Поз.	Обозначение	Наименование	Ед. изм.	Кол-во	Примечание
1	ИК/Т-М4П-А24-8,0	Кабель волоконно-оптический	м	900,0	демонтаж
2	ШТК	Шкаф домовой	шт.	3	демонтаж ПАО «Ростелеком»
3		Стойка ВКП	шт.	6	демонтаж
4	ОКСТМН-10-01-0,22-24-(2.7)	Кабель волоконно-оптический	м	629,90 00	монтаж

ТУ № 01/17/3194/25 - технические условия на вынос и переустройство кабелей связи ПАО «Ростелеком», проложенных методом ВКП и в кабельной канализации ПАО «МГТС», попадающих в границы проектирования объекта (от 24.02.2025 г.).

						125-0621-ОК-1-НСС8.1
1	-	Зам.	12-25		12.25	Жилой дом с инженерными сетями и благоустройством территории (со сносом зданий по адресам: ул. Судакова, д. 3, ул. Судакова, д. 5, ул. Судакова, д. 7) по адресу: г. Москва, внутригородское муниципальное образование Люблино, ул. Судакова, земельный участок 5 (Судакова ул., вл. 5) (Юго-Восточный административный округ)
Изм.	Кол.уч.	Лист	№ док.	Подпись	Дата	
Разработал		Меркулов			10.2025	Наружные сети связи. Вынос и переустройство кабелей связи ПАО «Ростелеком». Часть 1. Кластер 4.02
Проверил		Жмыхов			10.2025	Стадия: Р · Лист: 4 · Листов: -
ГИП		Жмыхов			10.2025	Ситуационный план волоконно-оптических сетей
						ООО "ВэллДан"

Согласовано
Взам. инв.N
Подпись и дата
Инв.N подл.

Формат А2